
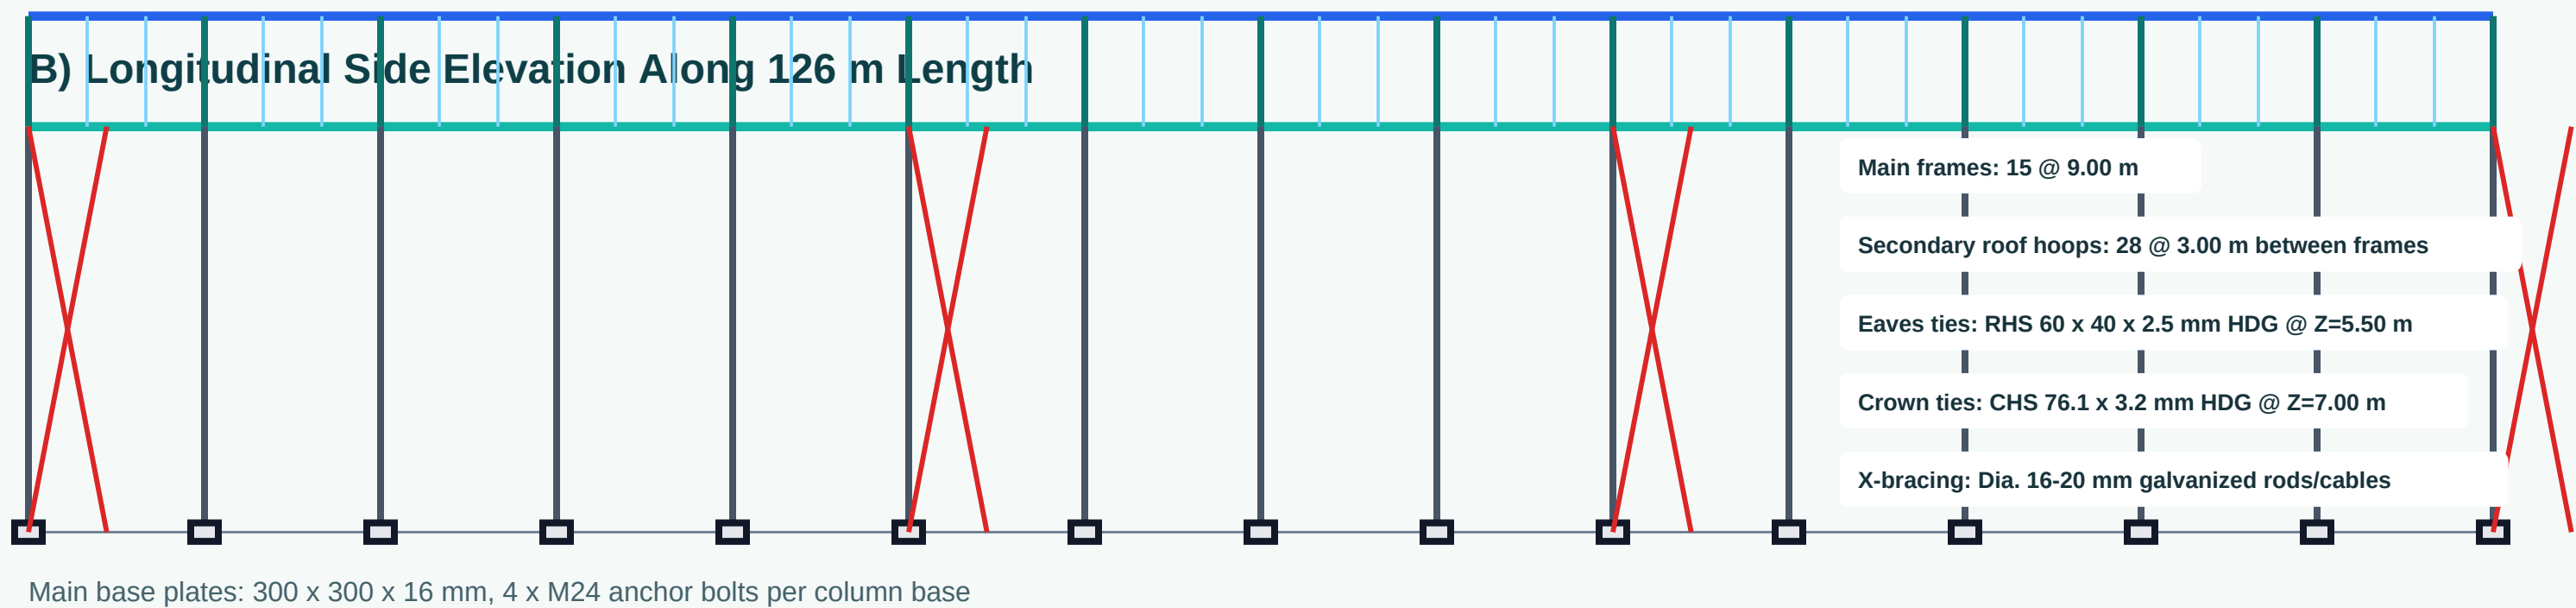


# Hydrofarms Adopted Greenhouse Steel Sections - Simplified Side View & Elevation

Production greenhouse 126 m x 36 m | Eaves 5.50 m | Ridge 7.00 m | Adopted preliminary structure

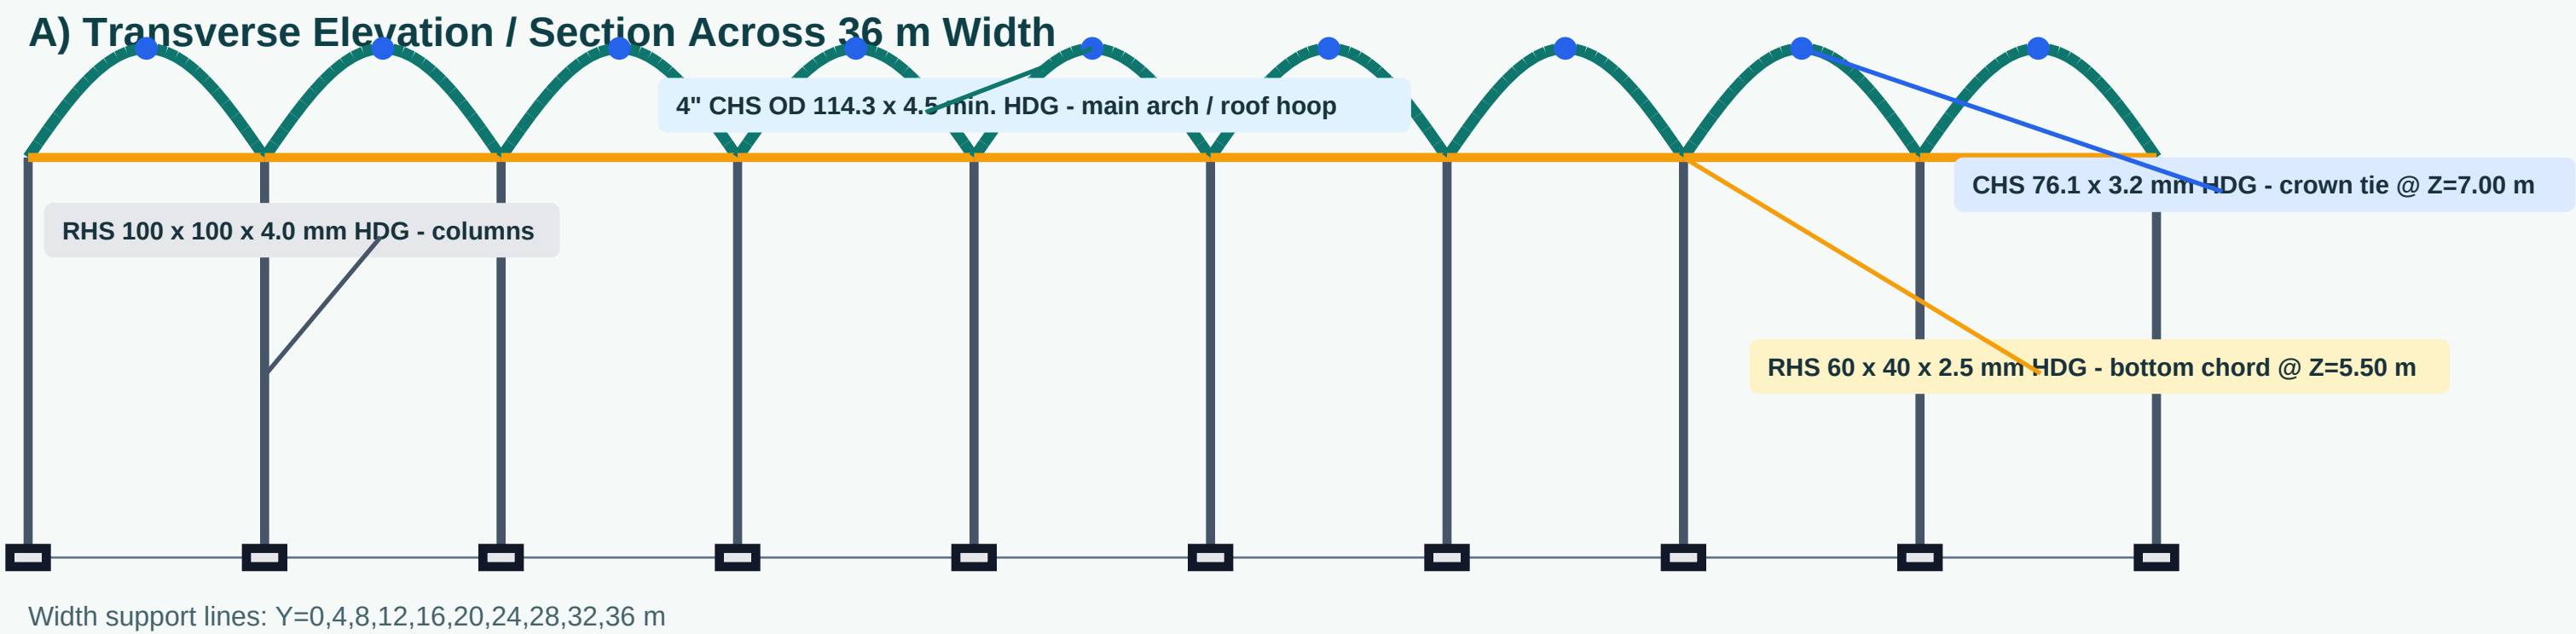

#### Color key

4" CHS OD 114.3 x 4.5 min. - main arches / roof hoops

RHS 100 x 100 x 4.0 - columns

RHS 60 x 40 x 2.5 - bottom chords

RHS 60 x 40 x 2.5 - eaves longitudinal ties

CHS 76.1 x 3.2 - crown ties

Dia. 16-20 mm - X bracing